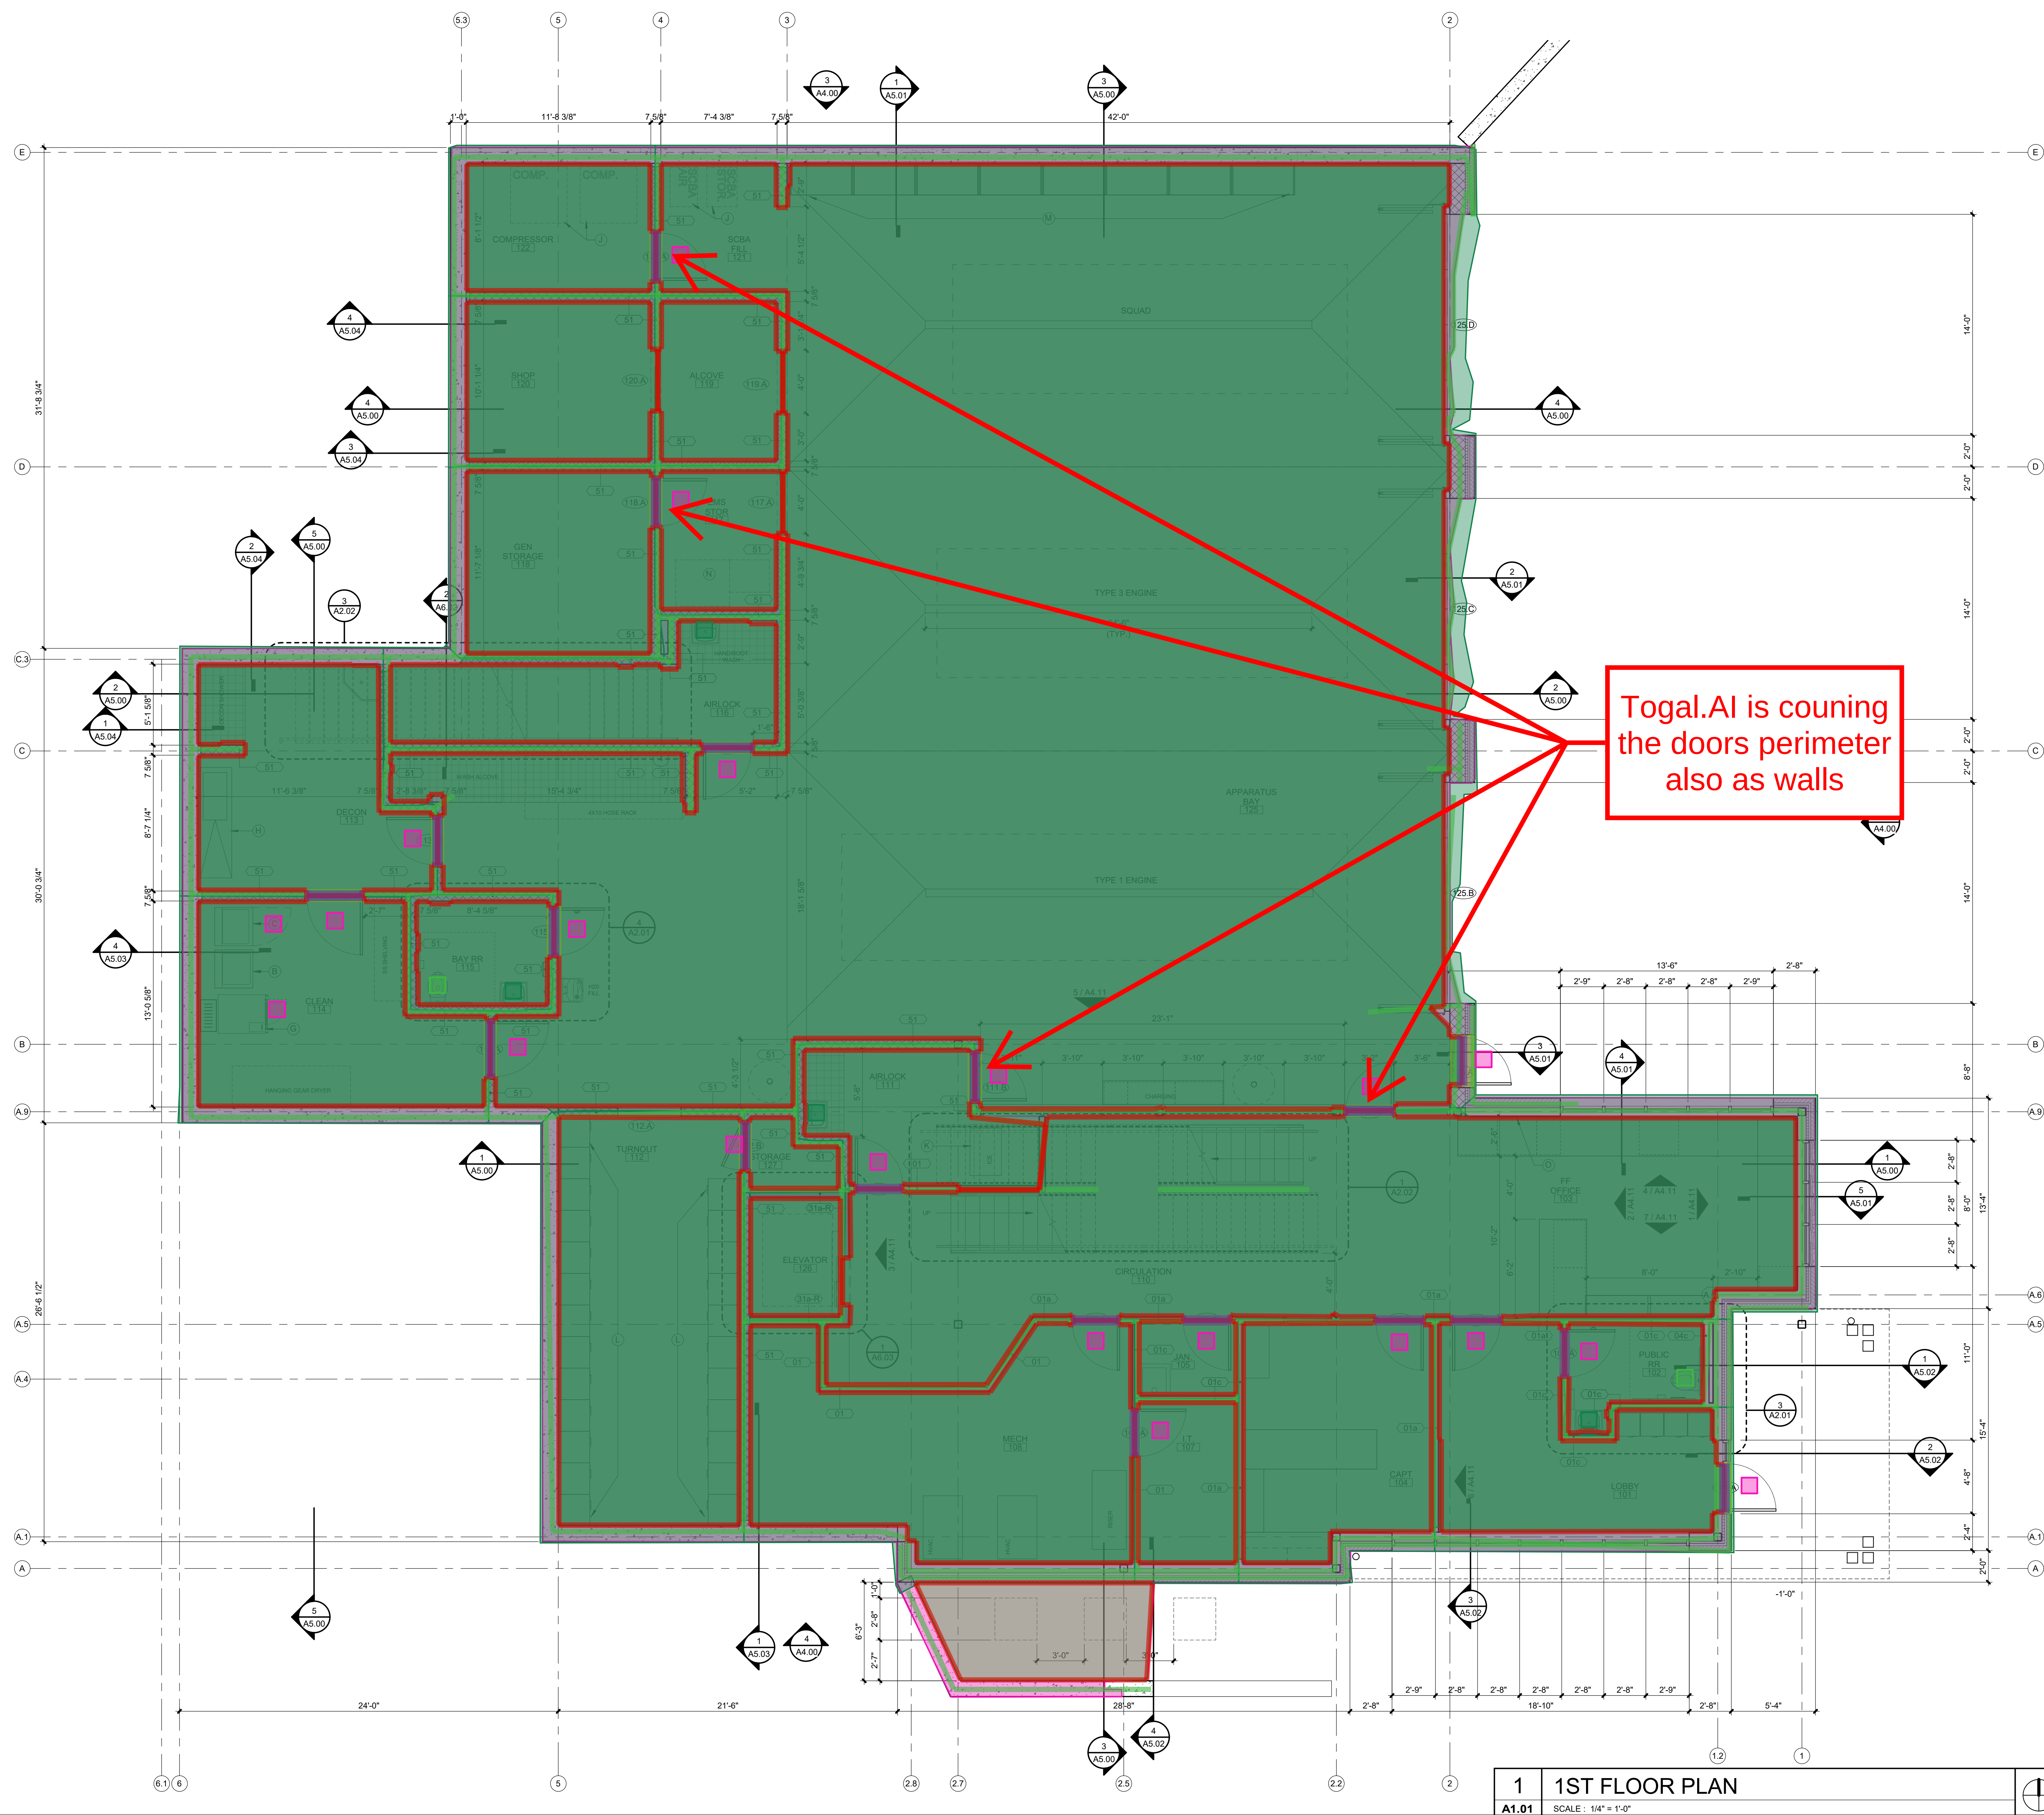


Total areas		
 Footprint	1	6,754 SF
 Net area	22	6,046 SF
 Doors area	19	44 SF
 Gross area	20	6,721 SF
 Gross Internal Area	...	206,238 SF
Total lines		
 Doors centerline	19	61 FT
 Wall centerline	146	1,038 FT
 Wall Perimeter	22	1,401 FT
Total counts		
 Toilet	2	2 EA
 Sink	4	4 EA
 Single Swing Door	21	21 EA

[illegible]

NOT FOR CONSTRUCTION

PROJECT TEAM	
ARCHITECT	FINKLE-Williams ARCHITECTURE
FIRE STATION CONSULTANT	TCA ARCHITECTURE
CIVIL	SK DESIGN GROUP
LANDSCAPE	SWT DESIGN
STRUCTURAL	BOB D. CAMPBELL
PLUMBING	LANKFORD FENDLE
MECHANICAL	LANKFORD FENDLE
ELECTRICAL	LANKFORD FENDLE
CONTRACTOR	TURNER CONSTRUCTION

C:\Users\kfooster\Documents\Olaith FS8-NEW_Central_R18_ellenfooster.nt