


Total areas		
	Fingerprint 1	734 SF
	Net area 14	617 SF
	Doors area 1	1 SF
	Gross area 12	664 SF
	Gross Internal Area (GIA)	12590 SF
Total lines		
	Doors centerline 1	2 FT
	Wall centerline 53	258 FT
	Wall Perimeter 14	383 FT
Total counts		
	Single Swing Door 14	14 EA

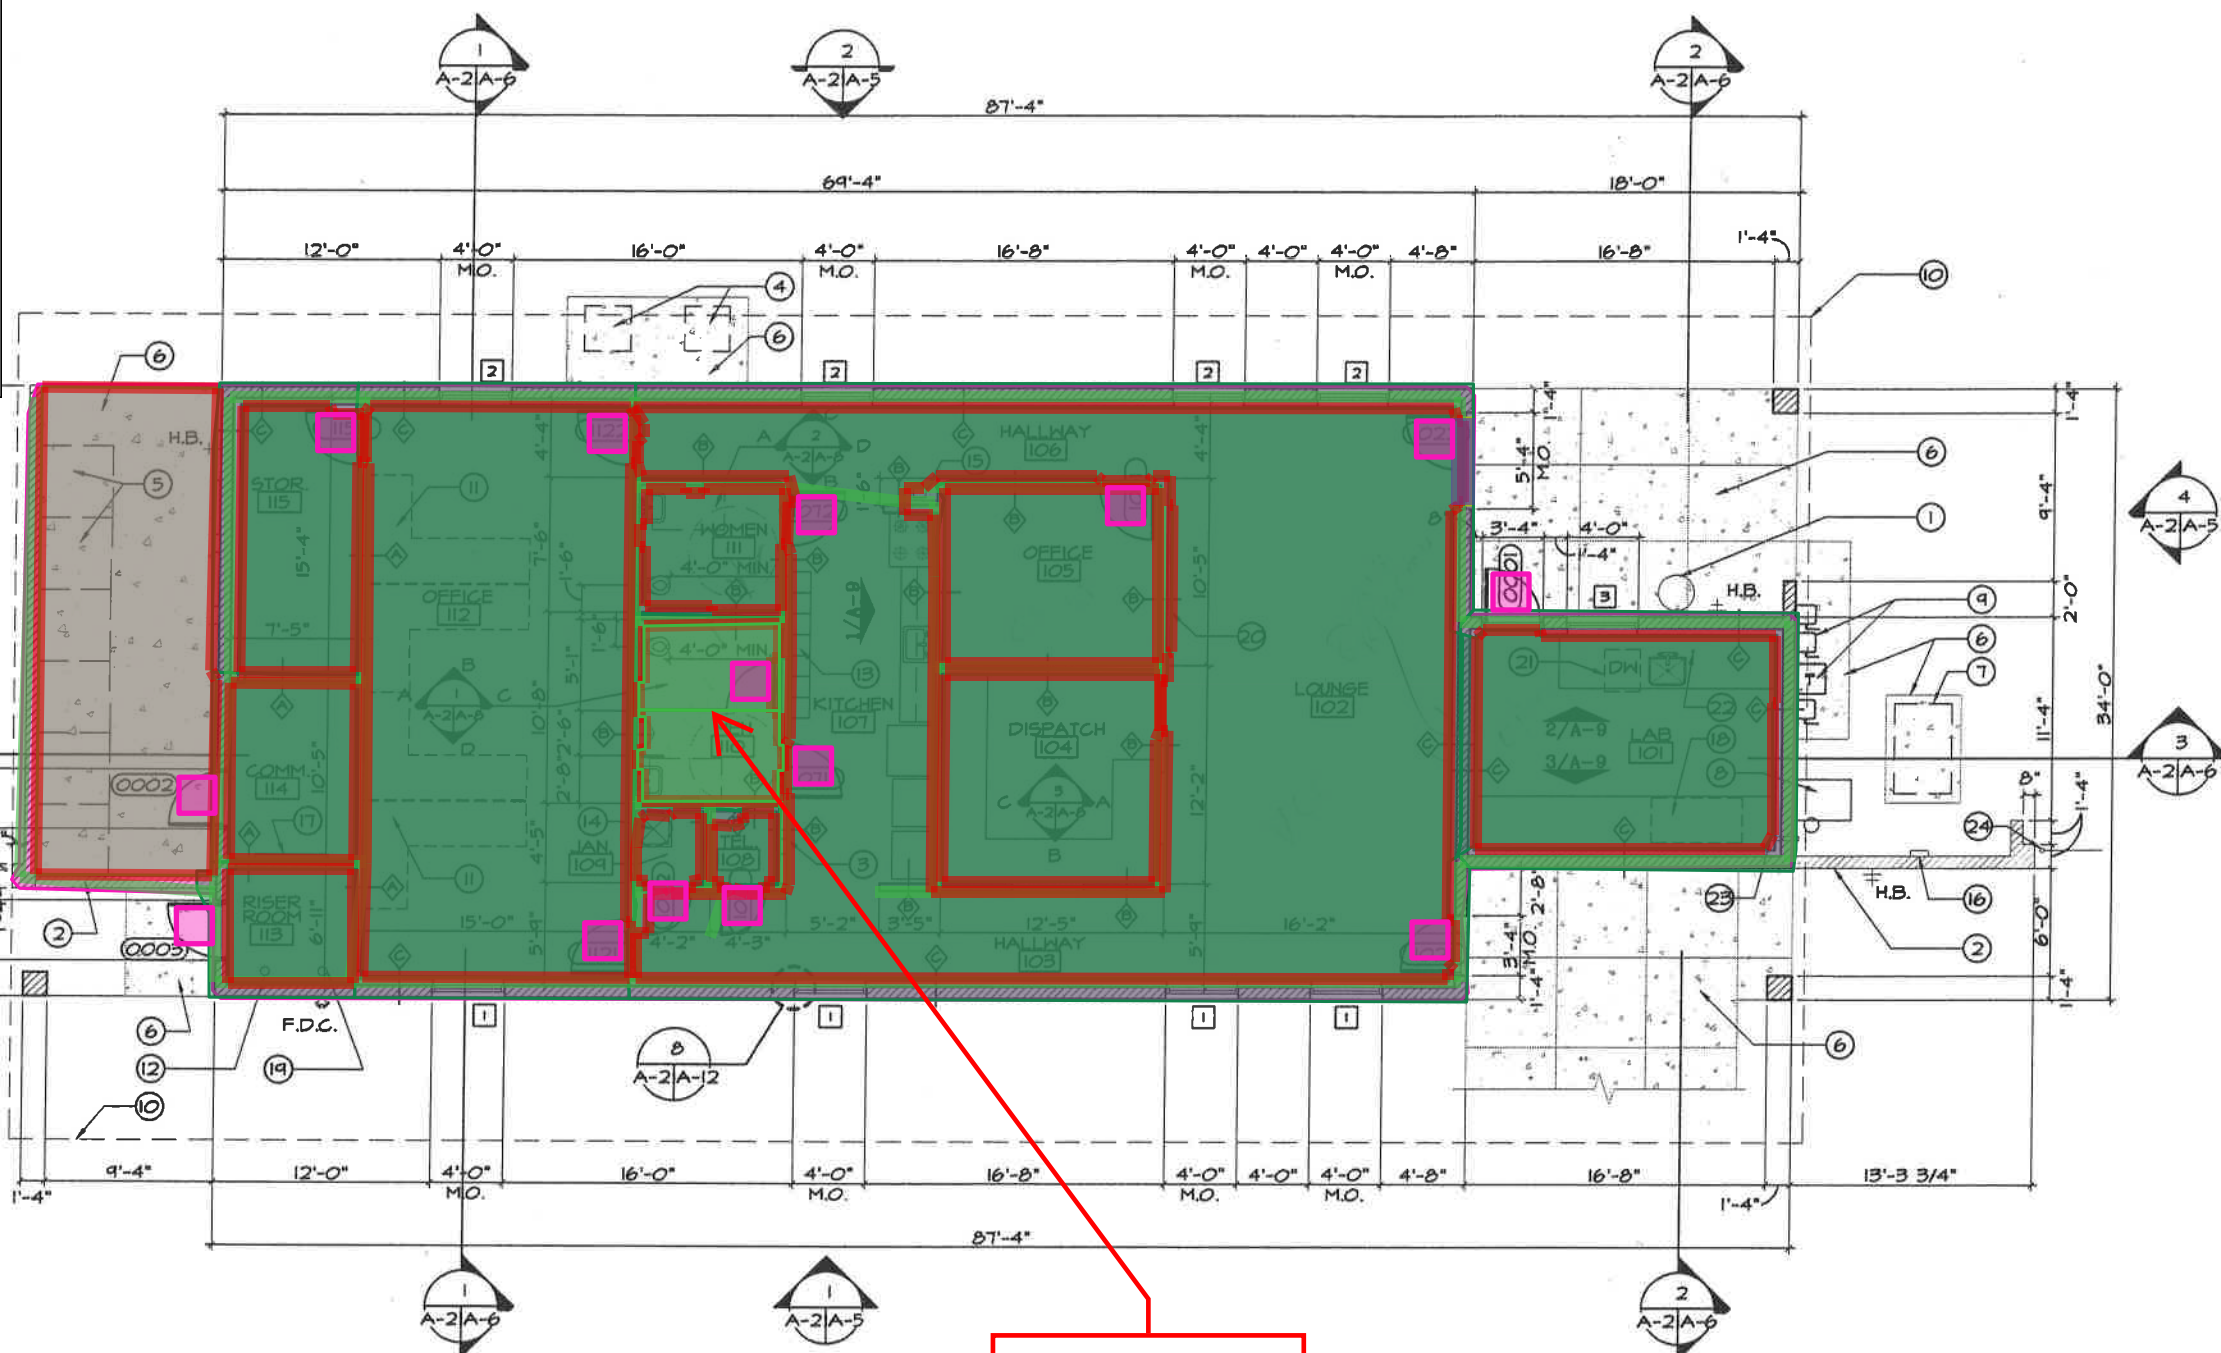

- ## FLOOR PLAN KEY NOTES
-
- ① OUTDOOR SHOWER AND EYEWASH
 - ② CMU SCREEN WALL- SEE ELEVATIONS FOR HEIGHT
 - ③ ELECTRICAL PANELS FLUSH MOUNTED IN 6" STUD WALL
 - ④ GROUND MOUNTED HEAT PUMP UNITS- REFER TO MECHANICAL DRAWINGS
 - ⑤ OUTDOOR PALLET RACK STORAGE
 - ⑥ CONCRETE PAD / WALK
 - ⑦ GROUND MOUNTED CONDENSING UNIT- REFER TO MECHANICAL DRAWINGS
 - ⑧ WALL MOUNTED EXHAUST FAN- REFER TO MECHANICAL DRAWINGS
 - ⑨ ELECTRICAL SERVICE- REFER TO ELECTRICAL DRAWINGS
 - ⑩ LINE OF ROOF OVERHANG
 - ⑪ SYSTEMS FURNITURE (N.I.C.)
 - ⑫ DOMESTIC WATER RISER- REFER TO PLUMBING DRAWINGS
 - ⑬ LOCKERS- REFER TO SPECIFICATIONS
 - ⑭ FLOOR MOP SINK WITH 20 GAL. WATER HEATER MOUNTED ABOVE- REFER TO PLUMBING DRAWINGS
 - ⑮ ELECTRIC DRINKING FOUNTAIN
 - ⑯ IRRIGATION CONTROLLER
 - ⑰ TELEPHONE MOUNTING BOARD
 - ⑱ 5' LONG EXHAUST HOOD
 - ⑲ FIRE SPRINKLER RISER
 - ⑳ BULLETIN BOARD (SUPPLIED BY OWNER, INSTALLED BY CONTRACTOR)
 - ㉑ DISHWASHER (SUPPLIED BY OWNER, INSTALLED BY CONTRACTOR)
 - ㉒ COUNTER MOUNTED EYEWASH
 - ㉓ 1" SLEEVE THRU WALL FOR FUEL DRAIN @ 30" A.F.F.
 - ㉔ SECURITY FENCE- 2"Ø SCHEDULE 40 PIPE IN CONCRETE FOOTING, REFER TO DETAIL 9/A-10. CENTER PIPE 1'-0" BACK FROM FACE OF MASONRY WALL

DEPARTMENT OF THE NAVY SAN DIEGO NAVAL FACILITIES ENGINEERING COMMAND CALIFORNIA SOUTHWEST DIVISION NAVAL FACILITIES		SATISFACTORY TO: DESIGN: DRAWN: CHECKED: FP:		DATE DATE DATE DATE DATE		APPROVED DATE PREP. BY		REVISIONS DESCRIPTION SYMBOL	
YU-0013R2 FUEL FARM BUILDING MARINE CORPS AIR STATION YUMA									
FLOOR PLAN									
SIZE D IF SHEET IS LESS THAN 22" X 34" IT IS A REDUCED PRINT- SCALE REDUCED ACCORDINGLY									
PWO. NO.									
PROJECT LOCATION									
CONSTR. CONTRACT NO.									
SPEC.									
NAVFAC DRAWING NO.									
SHEET 14 OF									
A-2									

 **1 FLOOR PLAN**
SCALE: 3/16" = 1'-0"

This 2 rooms where
no separated by
Togal.AI

WALL LEGEND		
TYPE	DETAIL	DESCRIPTION
		EXTERIOR 8" CMU WALL
 A	 2/A-II	INTERIOR PARTITION- 5/8" TYPE 'X' GYP. BD. BOTH SIDES 3-5/8" METAL STUD FRAMING, EXTEND TO ROOF STRUCTURE. PROVIDE R-II BATT INSULATION.
 B	 3/A-II	INTERIOR PARTITION- 5/8" TYPE 'X' GYP. BD. BOTH SIDES 3-5/8" METAL STUD FRAMING, EXTEND WALL TO 9'-6" A.F.F.. PROVIDE R-II BATT INSULATION.
 C	 4/A-II	INTERIOR PARTITION- FURR OUT CMU WALL W/ 5/8" TYPE 'X' GYP. BD. OVER 3-5/8" METAL STUD FRAMING. PROVIDE SPRAY-ON INSULATION. FRAMING AND INSULATION TO EXTEND TO BOTTOM OF ROOF TRUSSES. PROVIDE TYPE W.R. GYP. BD. AT RESTROOM SIDE OF INTERIOR PARTITIONS

100% SUBMITTAL	SHEET 14 OF A-2
----------------	--------------------

[illegible]